


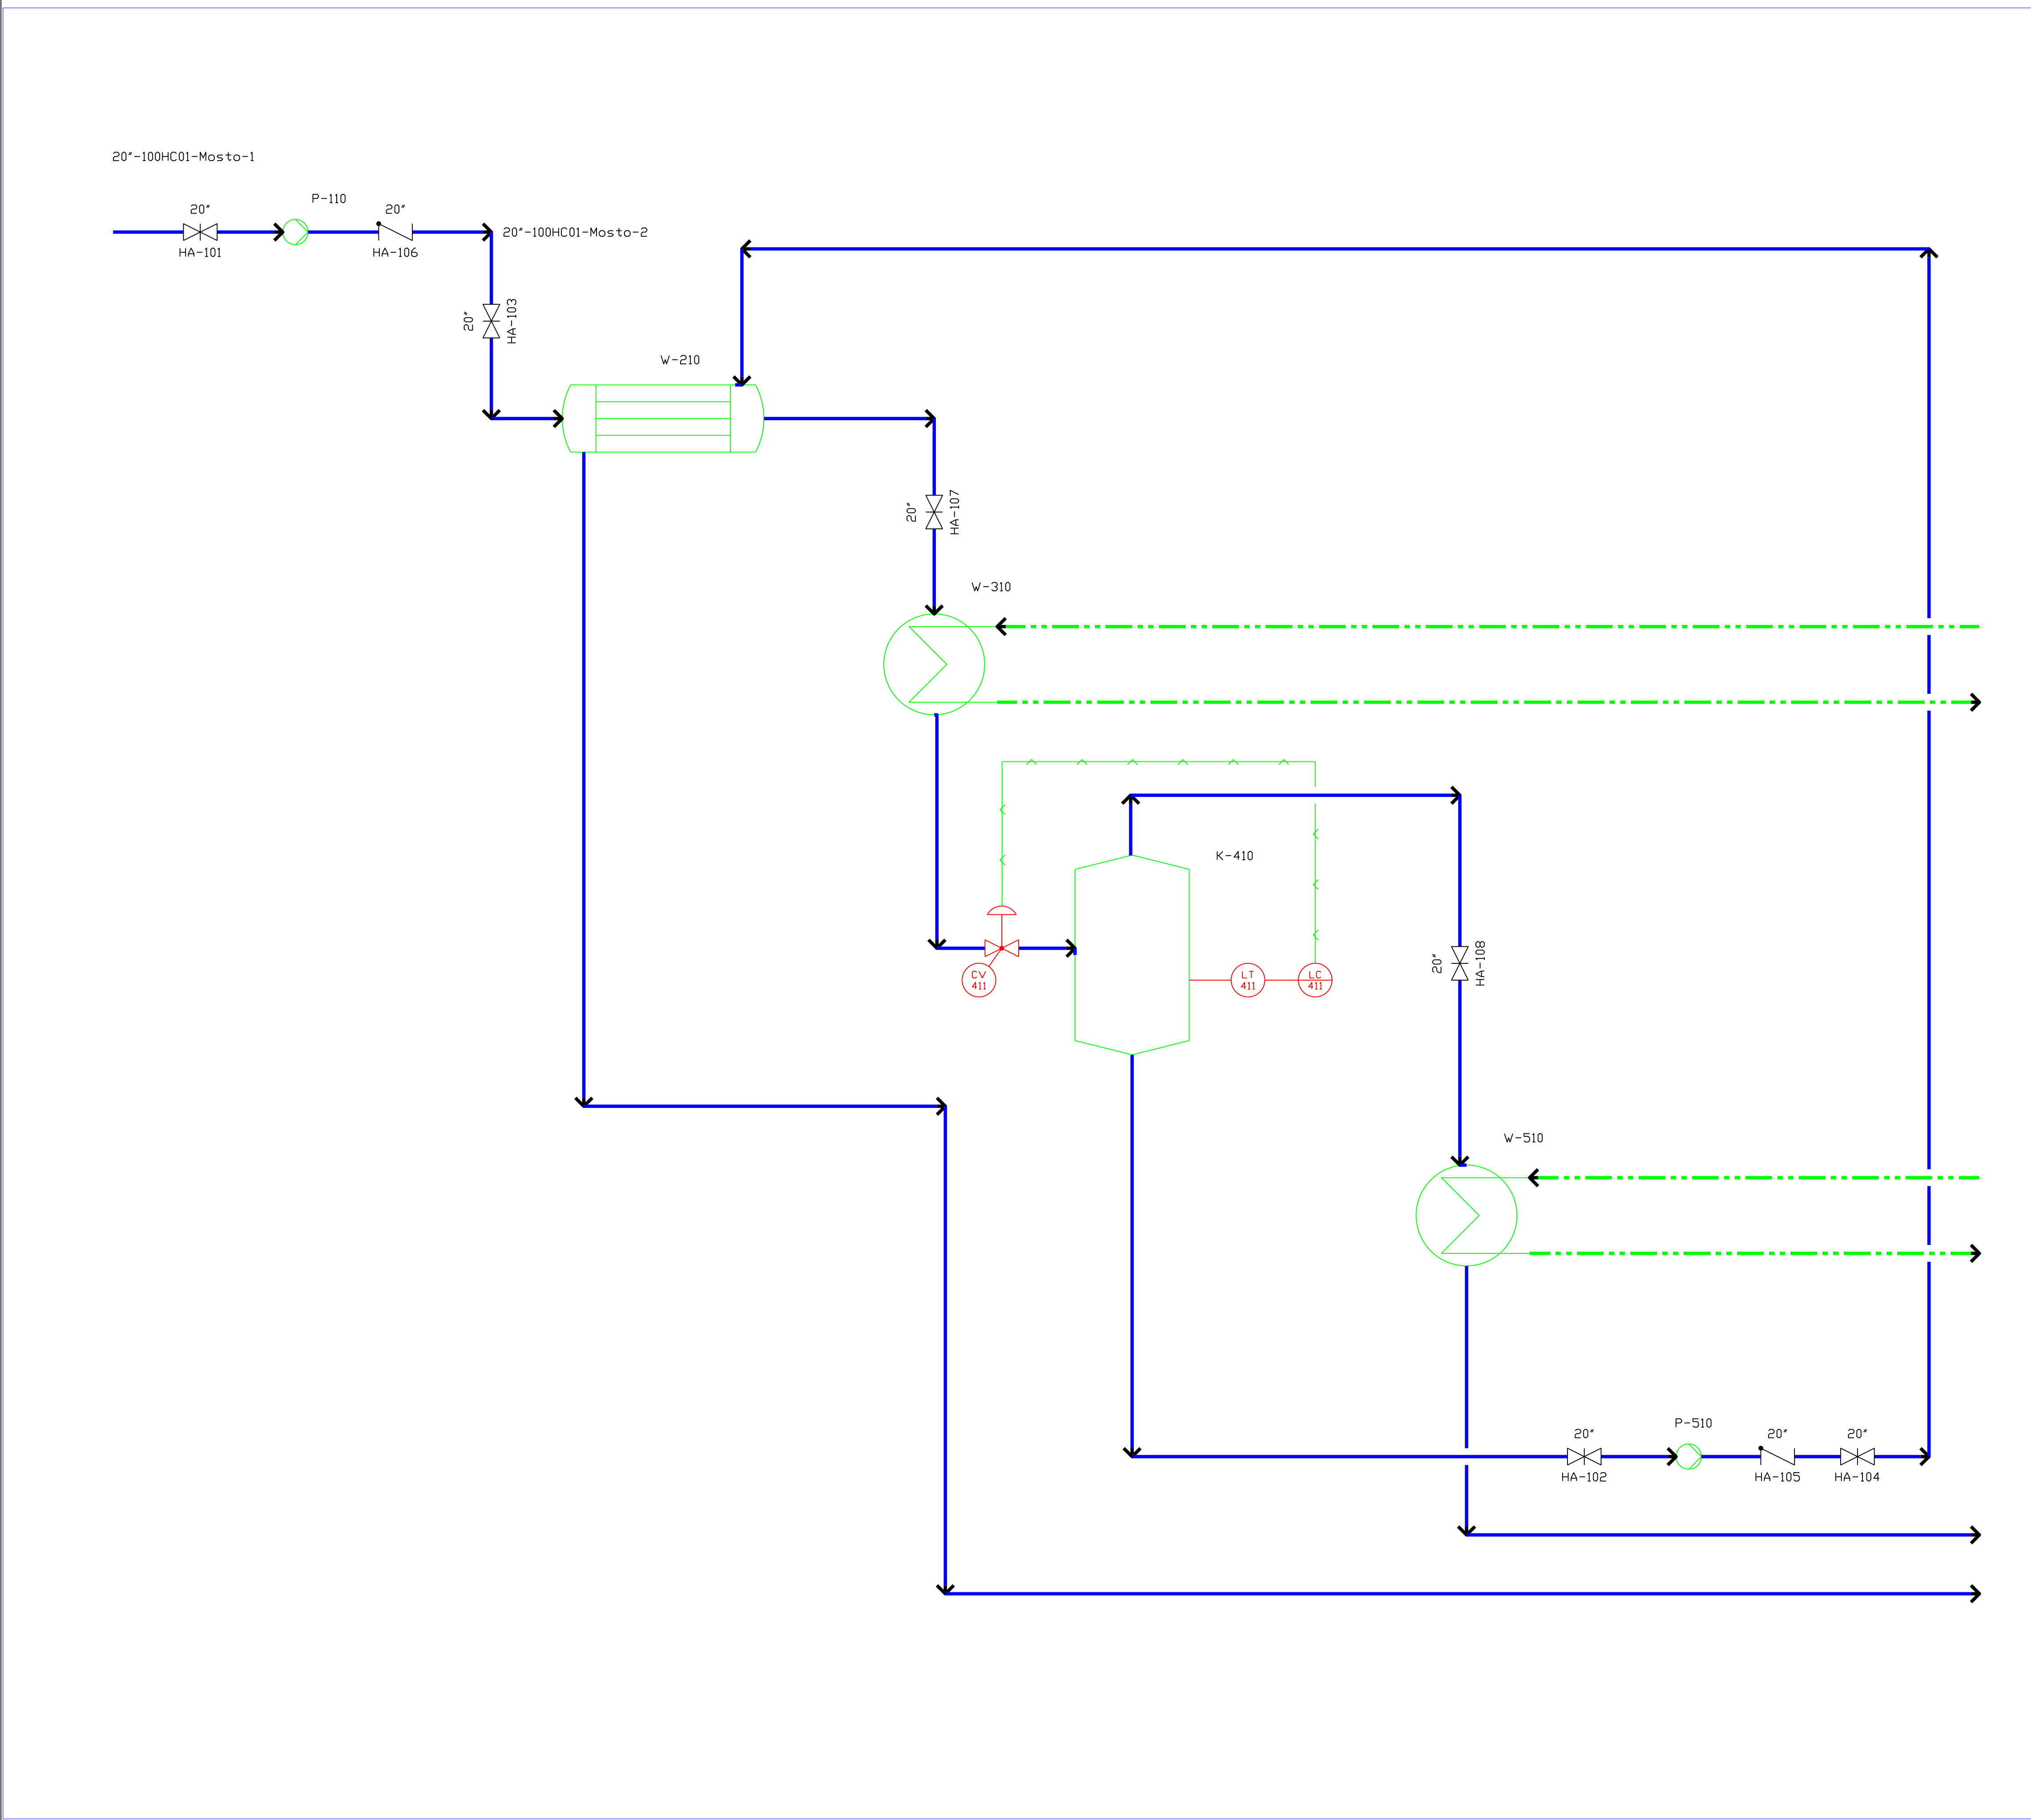

General Notes

- LT Transmisor de nivel
- LC Controlador de nivel en panel principal

No.	Revision/Issue	Date

Drawing Name

Diagrama de Tubería e Instrumentación (Principiantes)

Project Name and Address

Proceso de concentración de mosto

Area	100, 200, 300 y 400
Drawing Number	02
Author	Ing. Tania Bravo

